



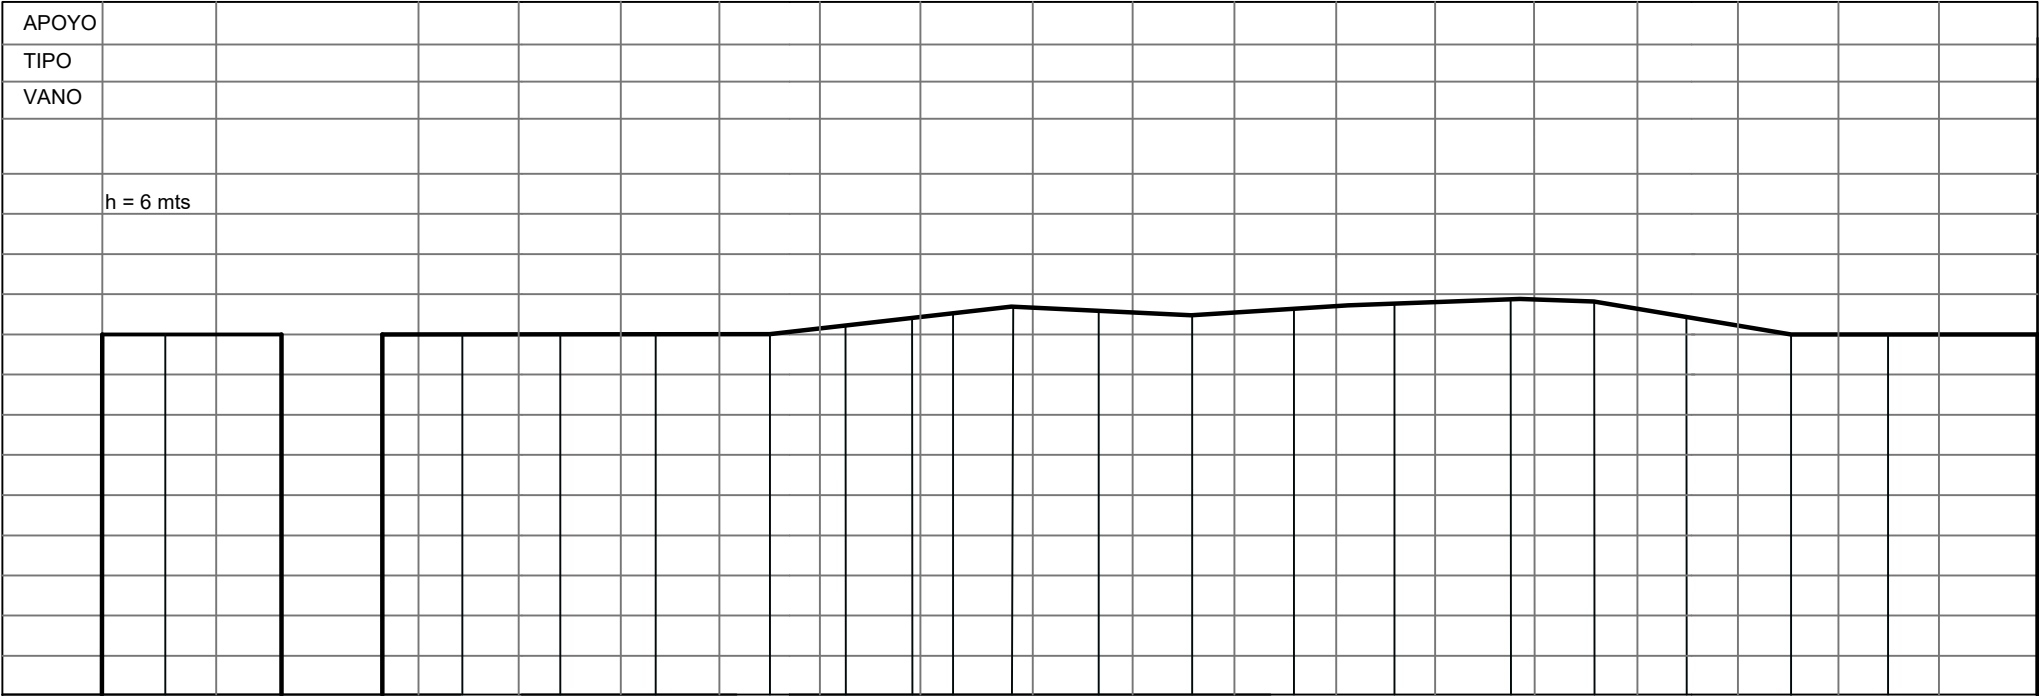

ESTACIONES	E0	E1	V1	V1	E2	E3	E4	E5	E6	E7	E8	E9	E10	E11	E12	E13	E14	E15	E16	E17	E18													
C. TERRENO	200.10	200.10	200.10	200.10	200.10	200.10	200.10	200.10	200.05	200.04	207.37	210.08	211.49	213.38	216.73	218.30	213.06	212.67	211.14	213.38	214.72	216.19	217.57	218.63	218.49	218.83	218.83	214.78	210.18	205.32	200.34	200.34	200.34	200.34
D. PARCIALES		100 mts	84.92 mts	36.04 mts	100 mts	100 mts	100 mts	100 mts	100 mts	100 mts	100 mts	100 mts	100 mts	100 mts	100 mts	100 mts	100 mts	100 mts	100 mts	100 mts	100 mts	100 mts	100 mts	100 mts	100 mts	100 mts	100 mts	100 mts	100 mts	100 mts	100 mts	100 mts	100 mts	
PROGRESIVA	0+000.00	0+100.00	0+184.92	0+220.96	0+320.96	0+420.96	0+520.96	0+620.96	0+720.96	0+820.96	0+920.96	1+020.96	1+120.96	1+220.96	1+320.96	1+420.96	1+520.96	1+620.96	1+720.96	1+820.96	1+920.96	2+020.96	2+120.96	2+220.96	2+320.96	2+420.96	2+520.96	2+620.96	2+720.96	2+820.96	2+920.96	3+020.96	3+120.96	3+220.96
PROPIETARIOS																																		

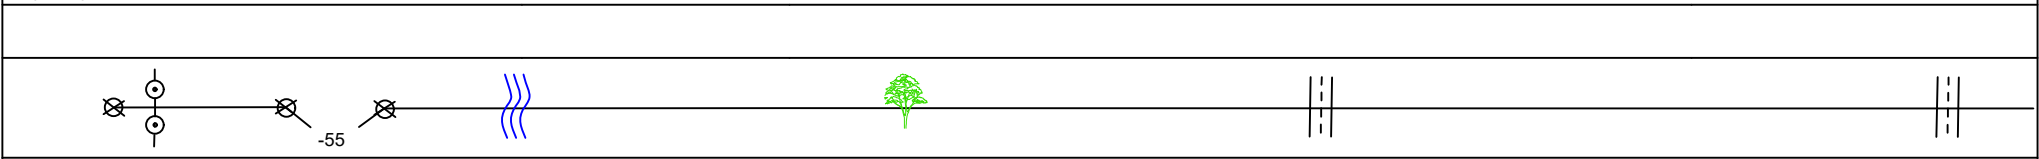

Autor: MARIENE MORA 20397639	Línea de 115kv S/E PEÑA LARGA - S/E GUANARE	
	Tramo I 1.8 km	
Escala	V:1-500	Enero 2021
	H:1-2000	Trabajo de Grado